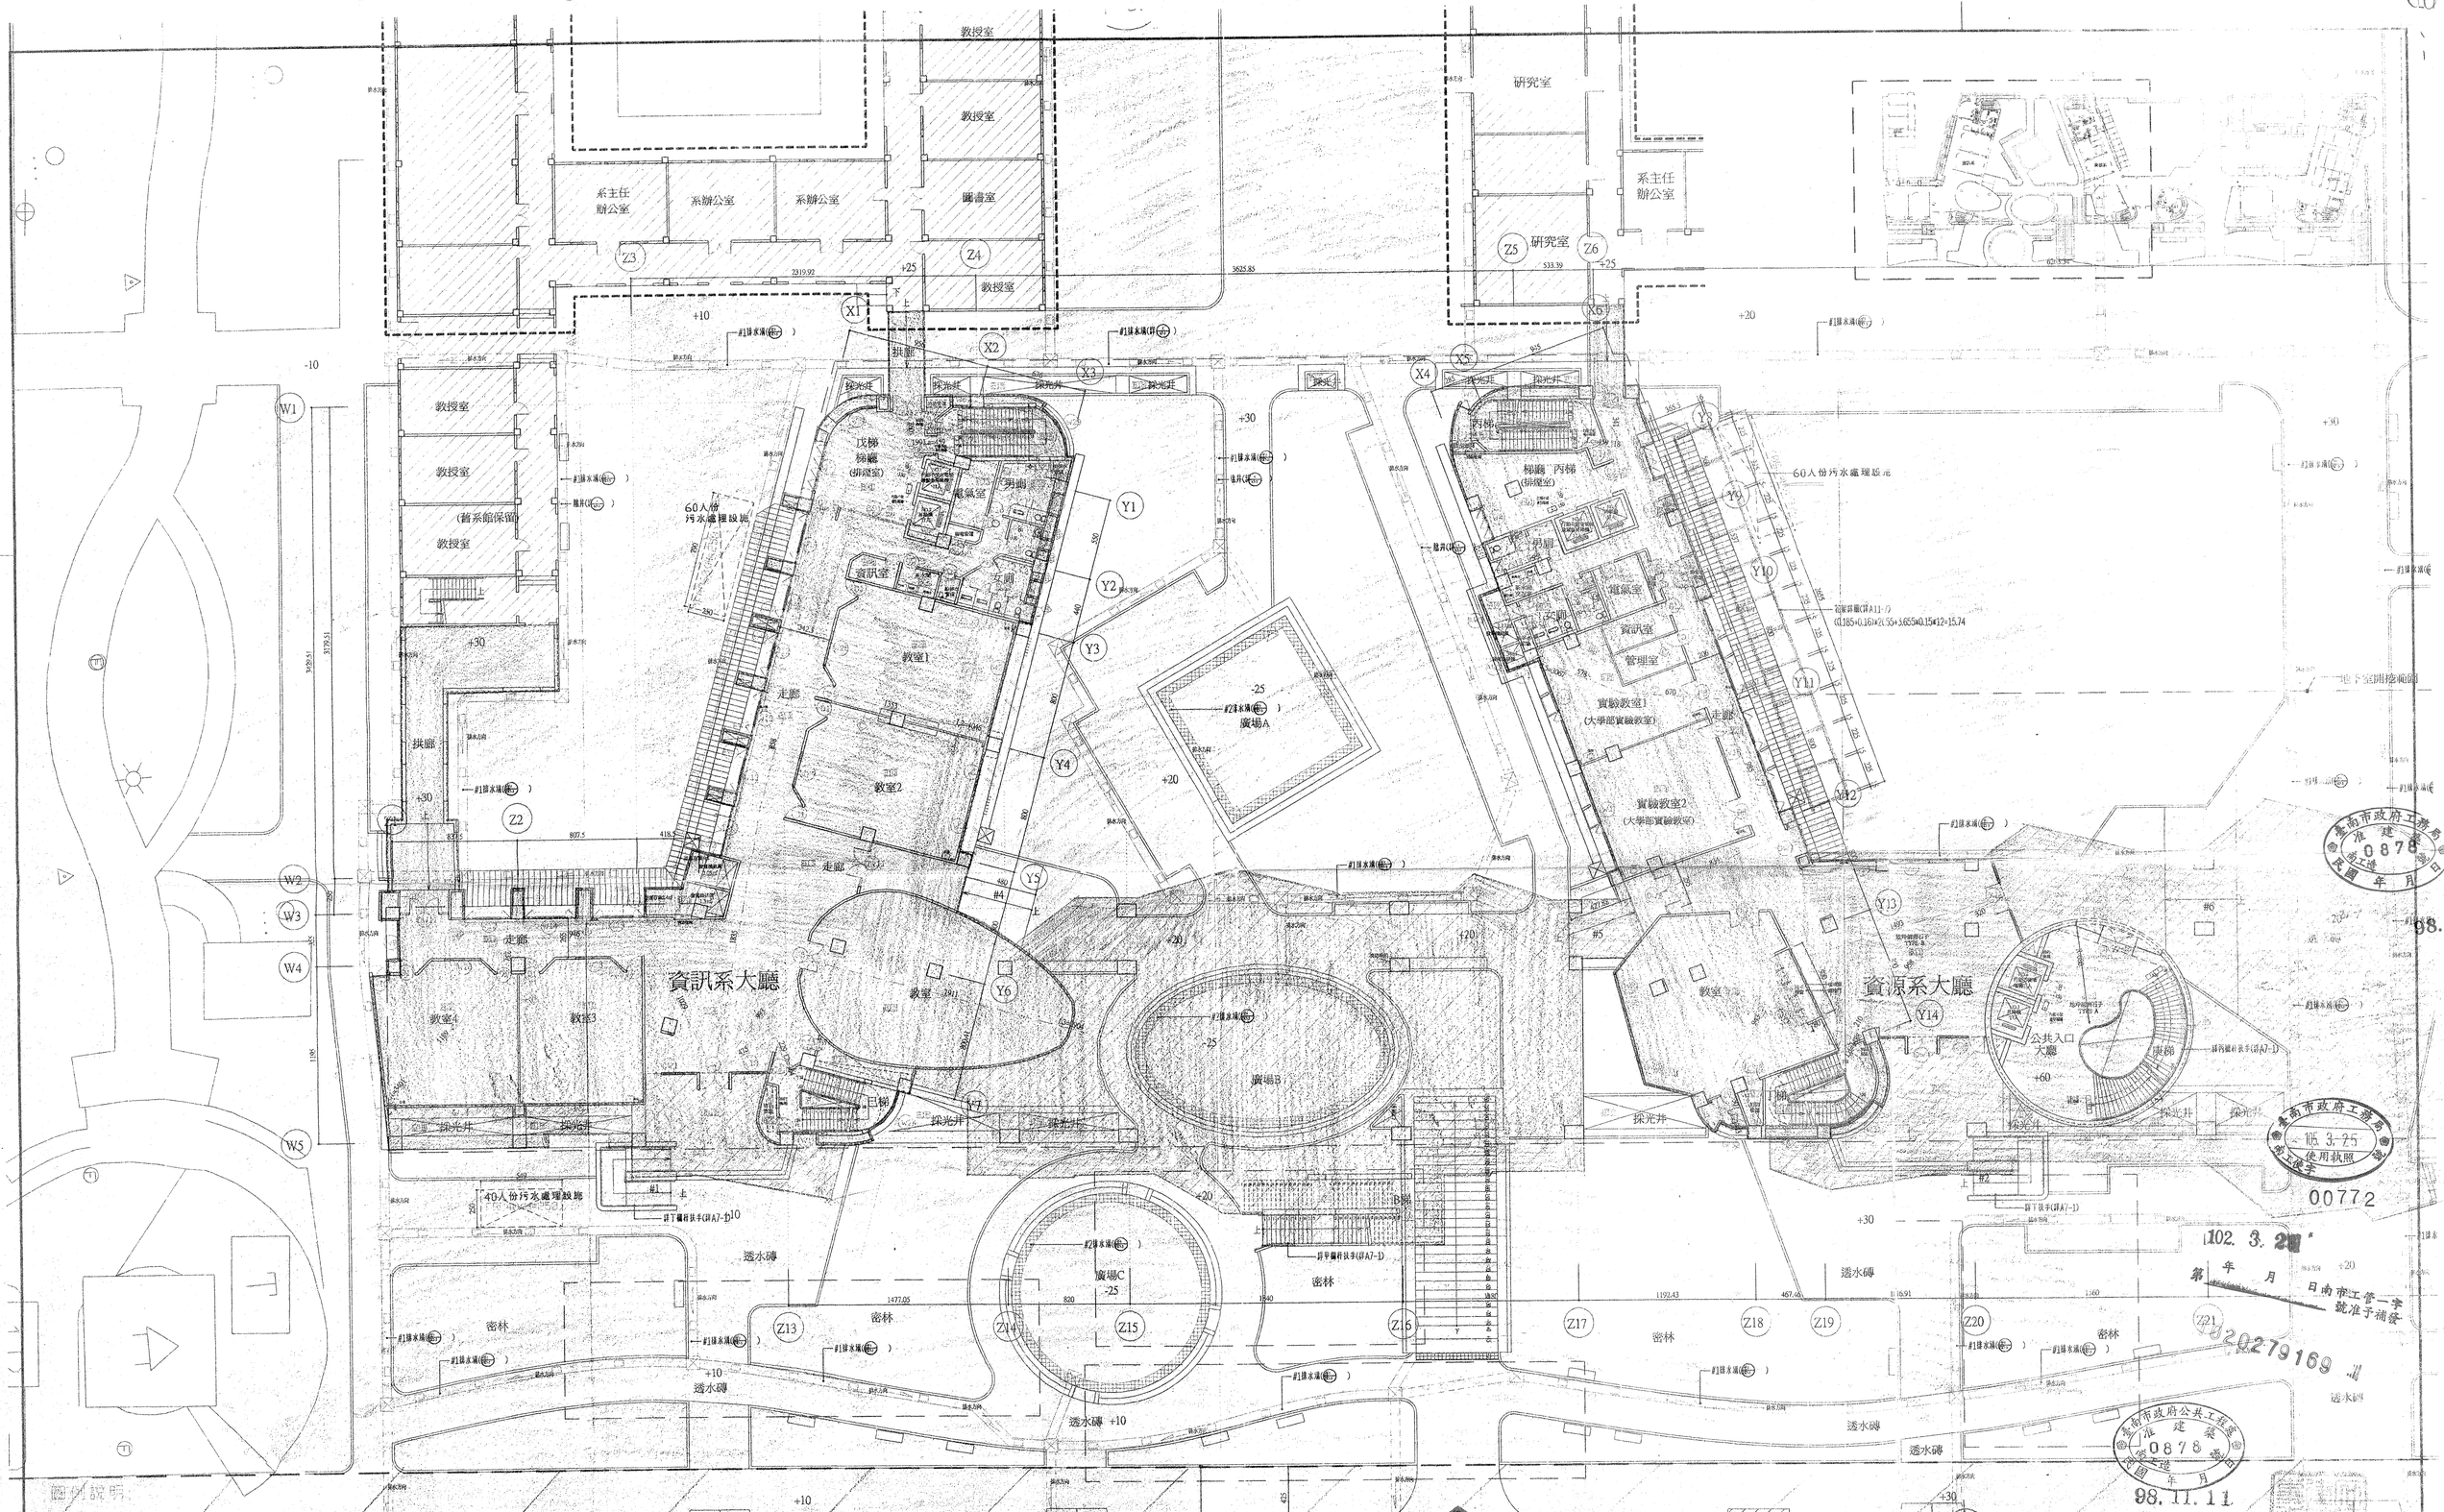

修正	日期	說明	核准	繪圖		設計		比例尺	1/200
				核對		核准		日期	98.11.10

石昭永建築師事務所
建築師 石昭永
所址 台南市東安路298號2樓
TEL 06-2370370
FAX 06-2370373

簽章:

工程名稱	成功大學成功校區 東側教學舍後期更新整建工程	業務號	圖號	張號
圖別	一層平面圖--1		A2-6	18-89